


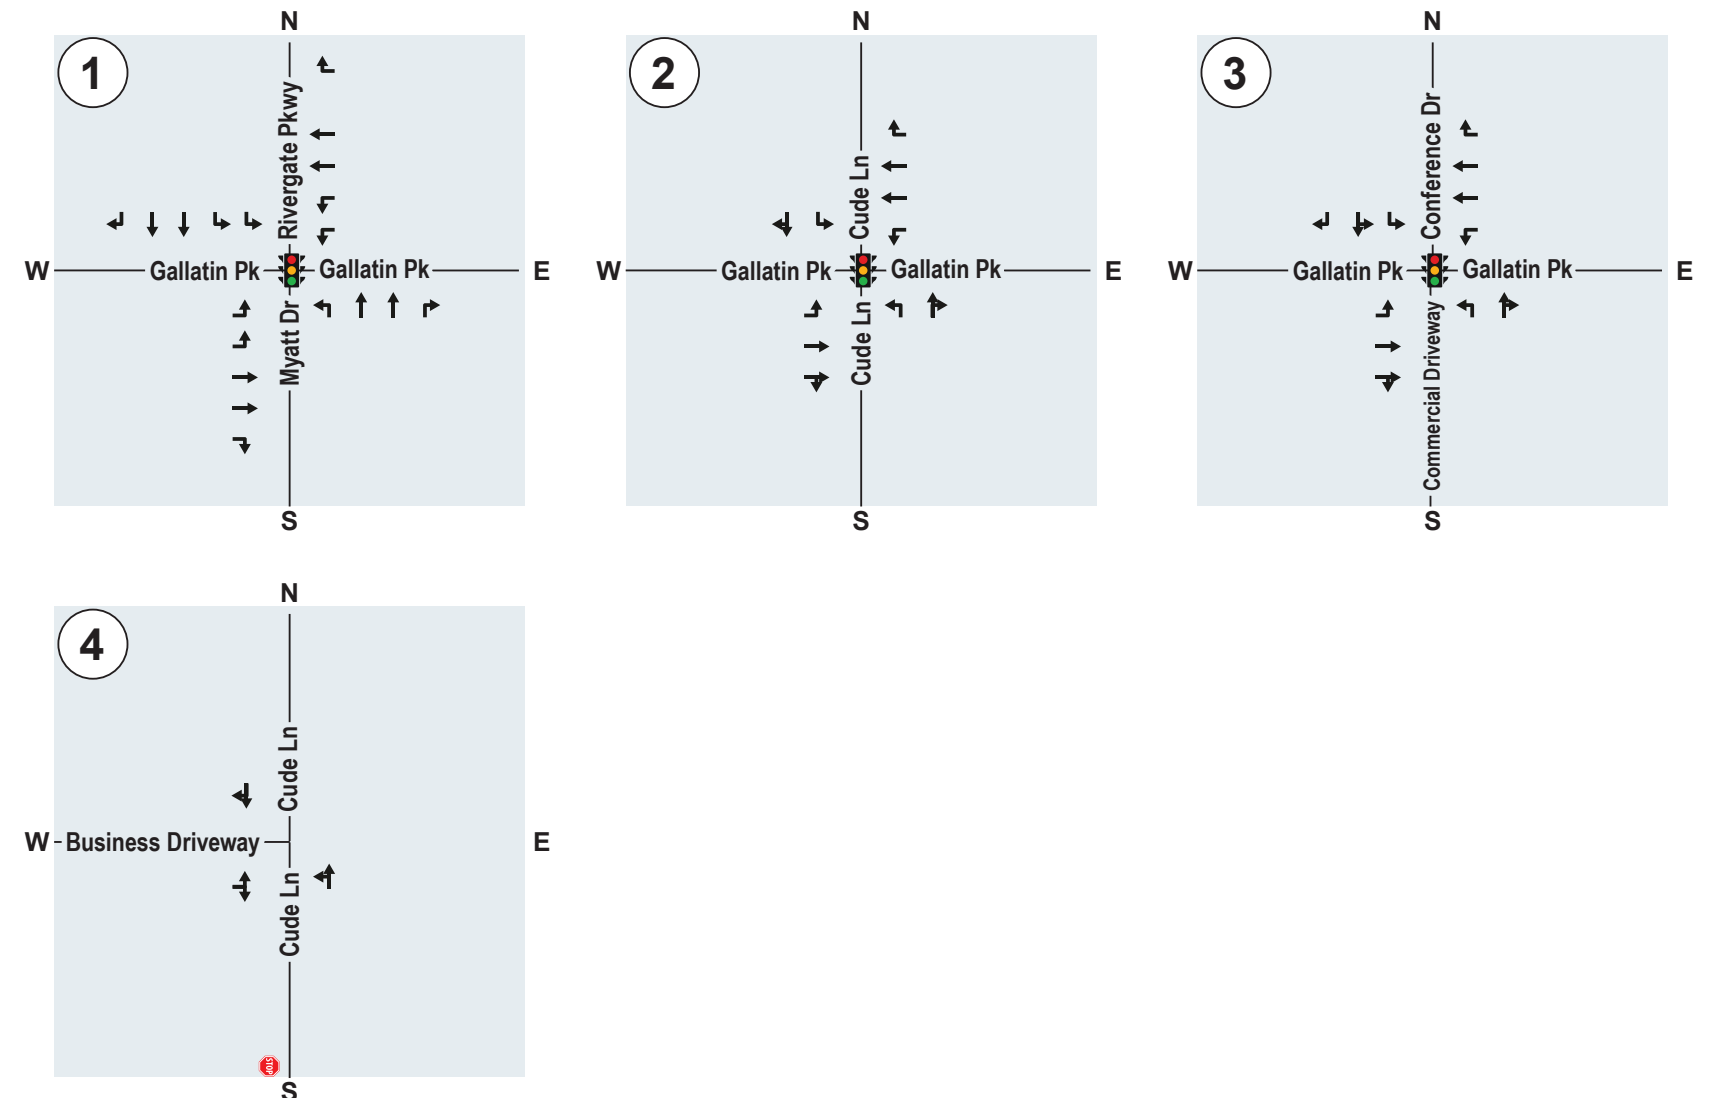



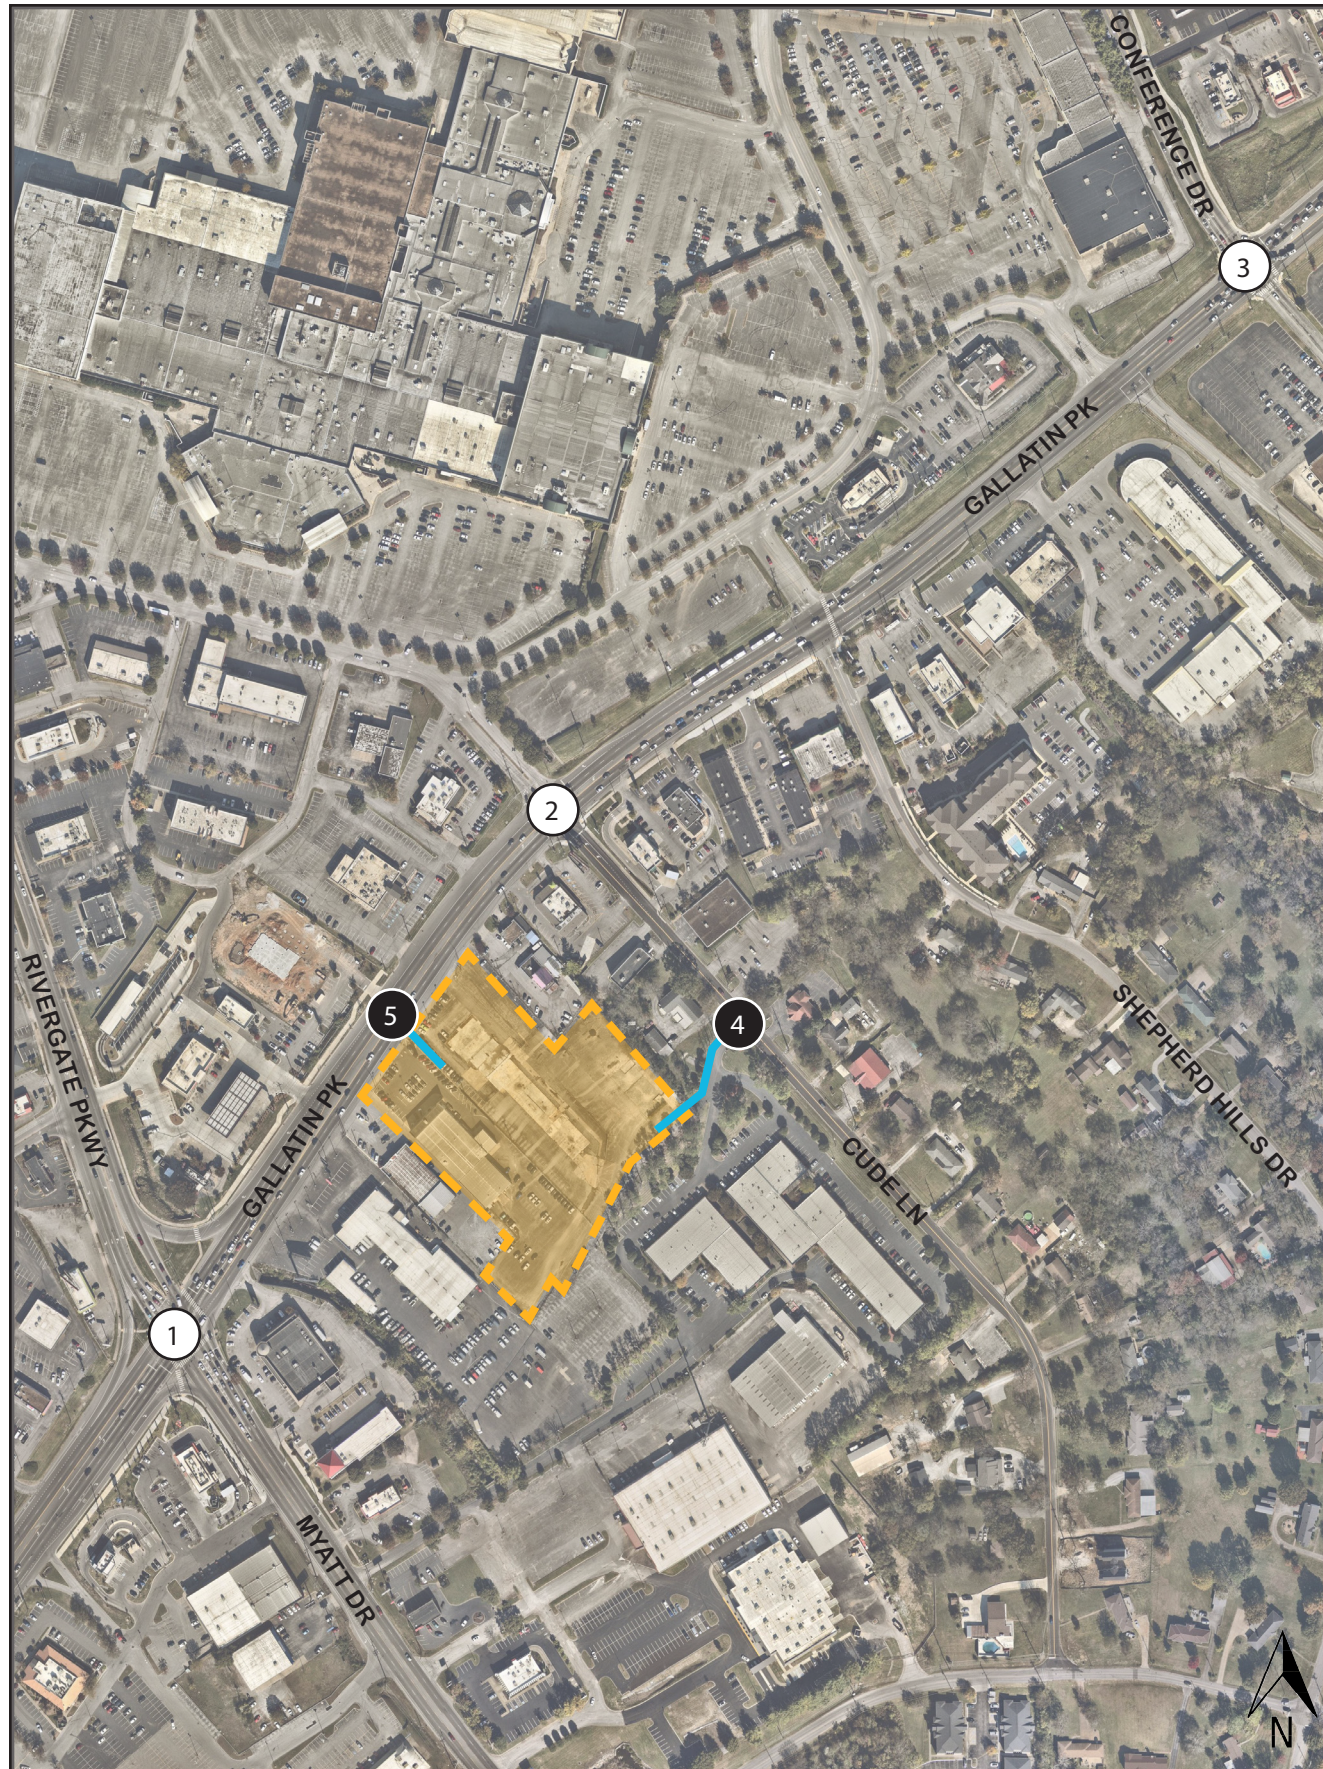


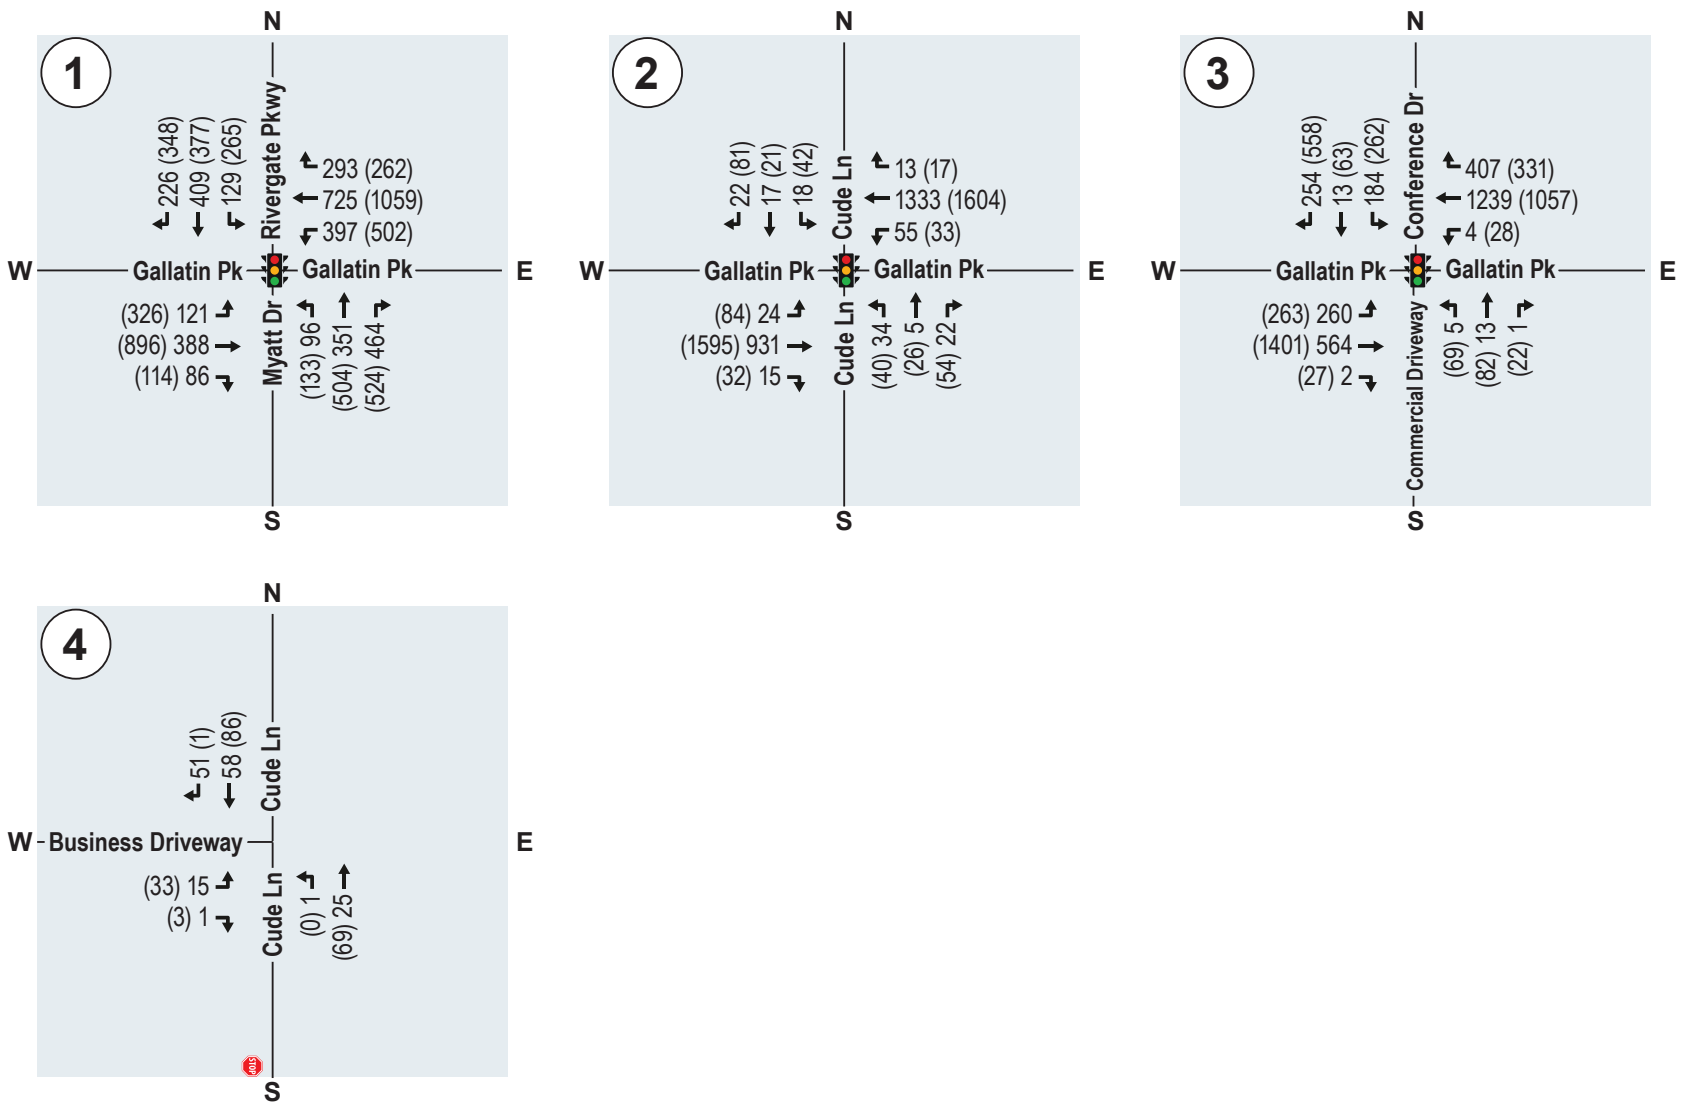



LEGEND			
(X)	Signalized Intersection ID		Existing Traffic Signal
(X)	Unsignalized Intersection ID		Existing Stop Sign
			Existing Lane Configuration

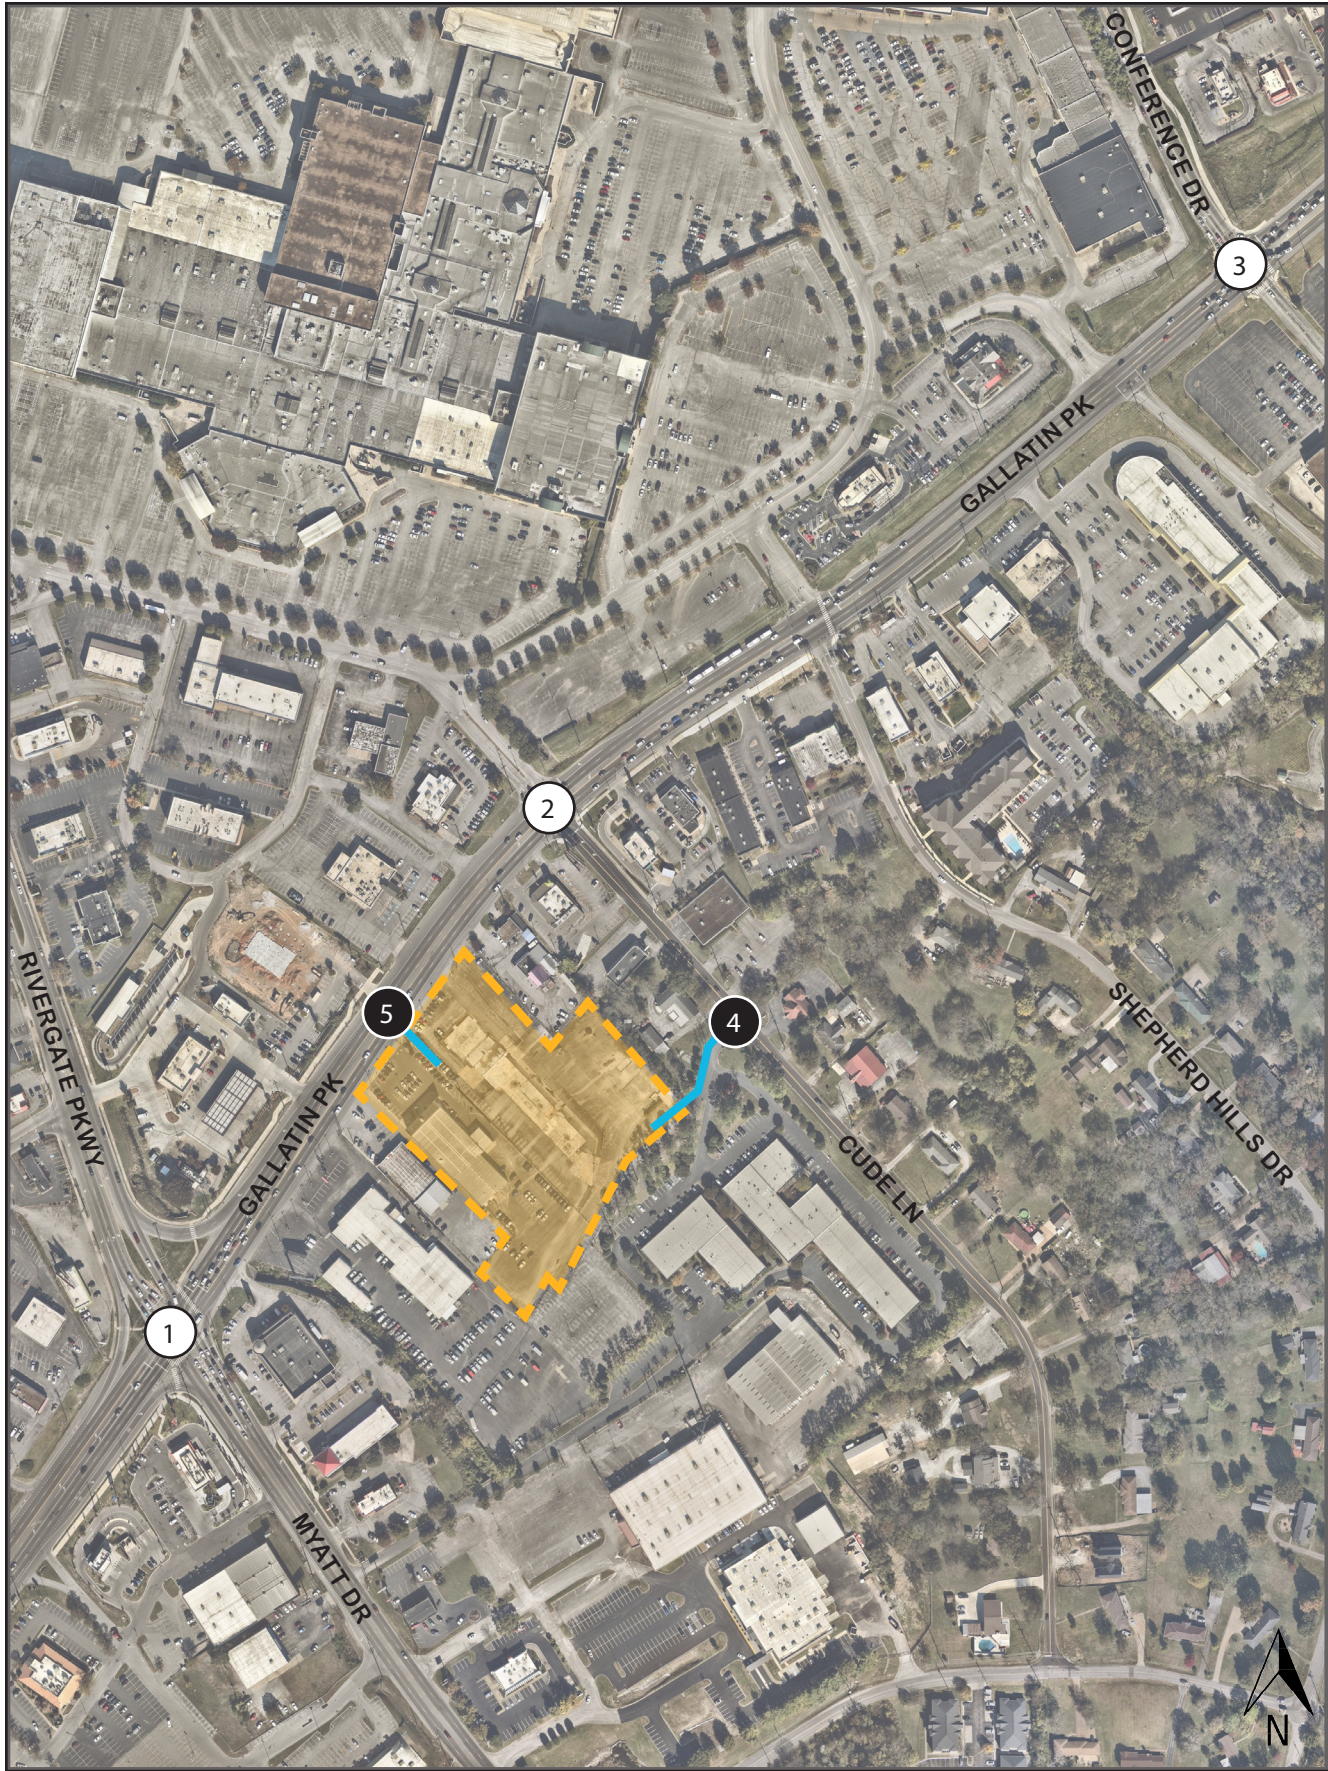



LEGEND		Signalized Intersection ID		Existing Traffic Signal	XX	AM Peak Hour Traffic Volumes
		Unsignalized Intersection ID		Existing Stop Sign	(XX)	PM Peak Hour Traffic Volumes
		Turning Movement				

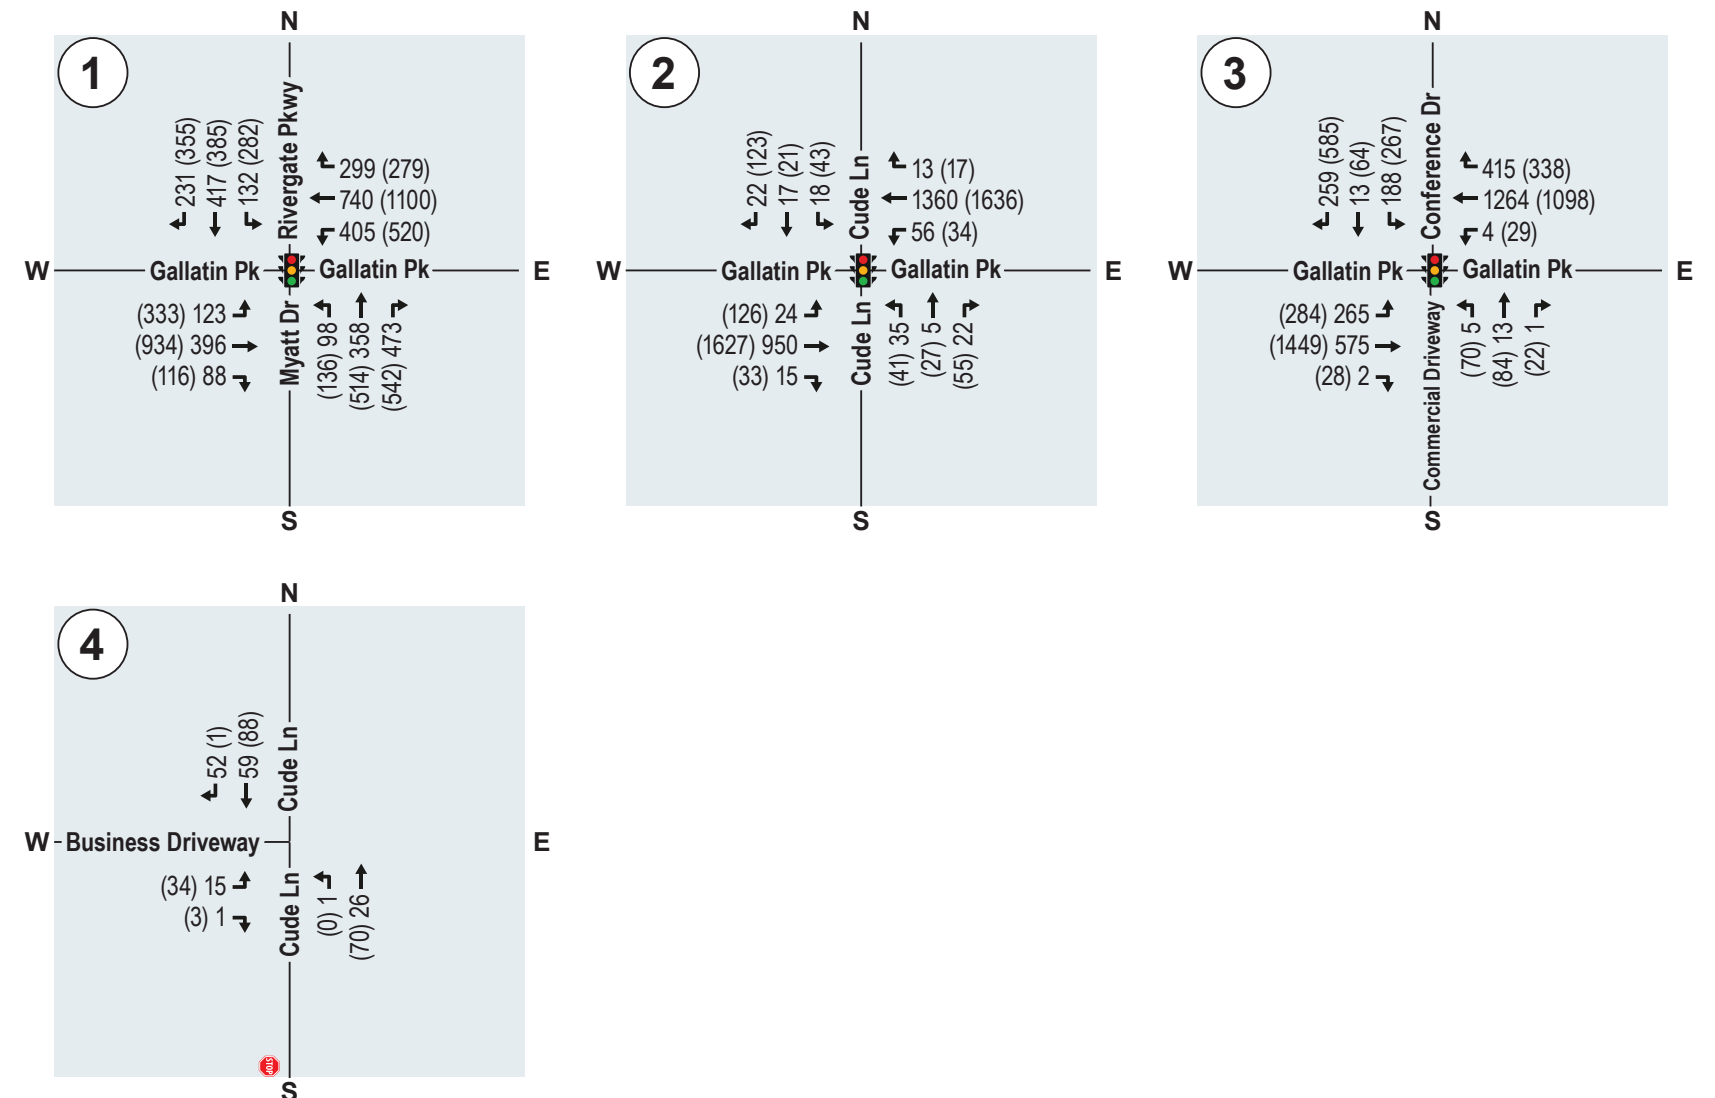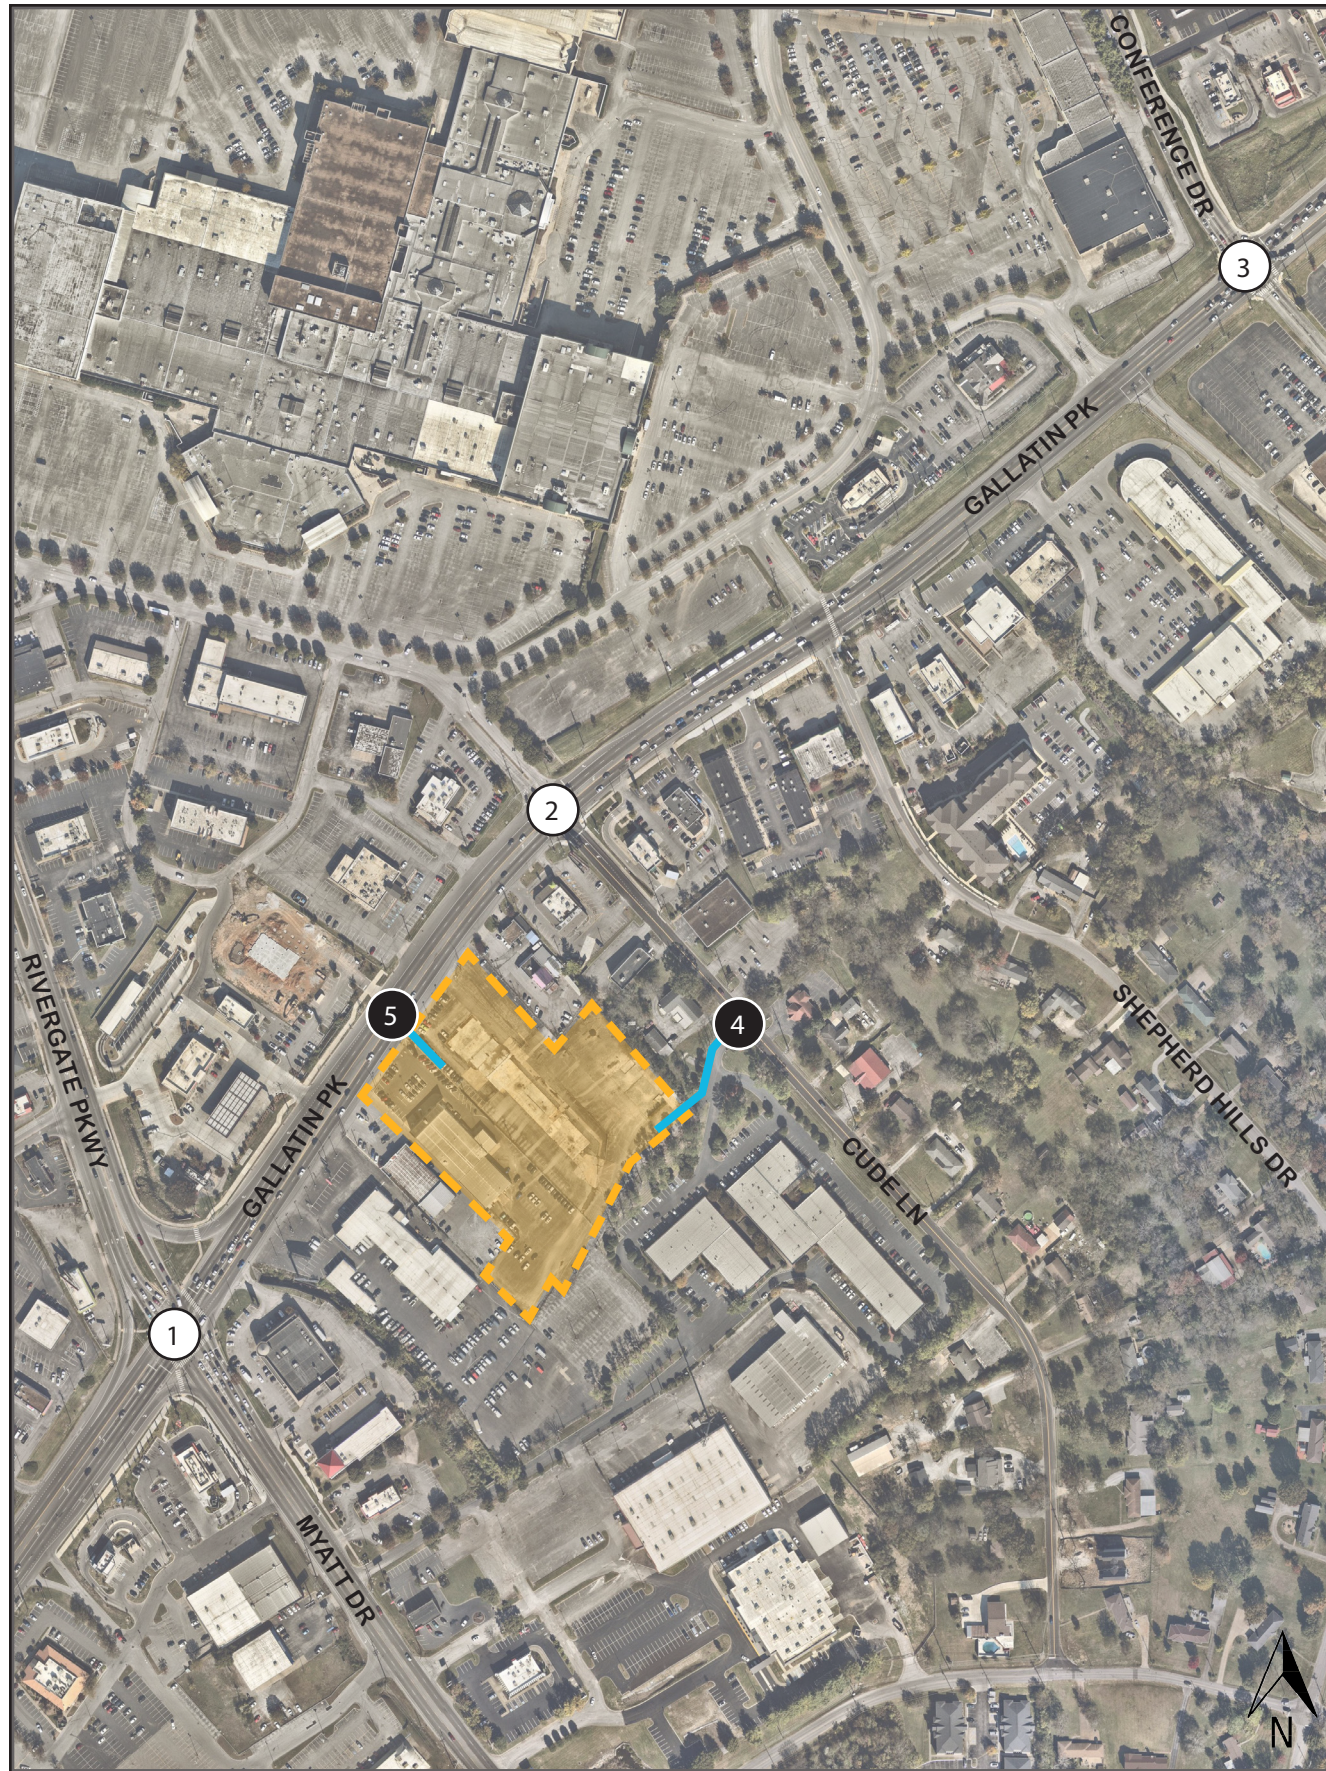



LEGEND		Signalized Intersection ID		Existing Traffic Signal	XX	AM Peak Hour Traffic Volumes
		Unsignalized Intersection ID		Existing Stop Sign	(XX)	PM Peak Hour Traffic Volumes
		Turning Movement				

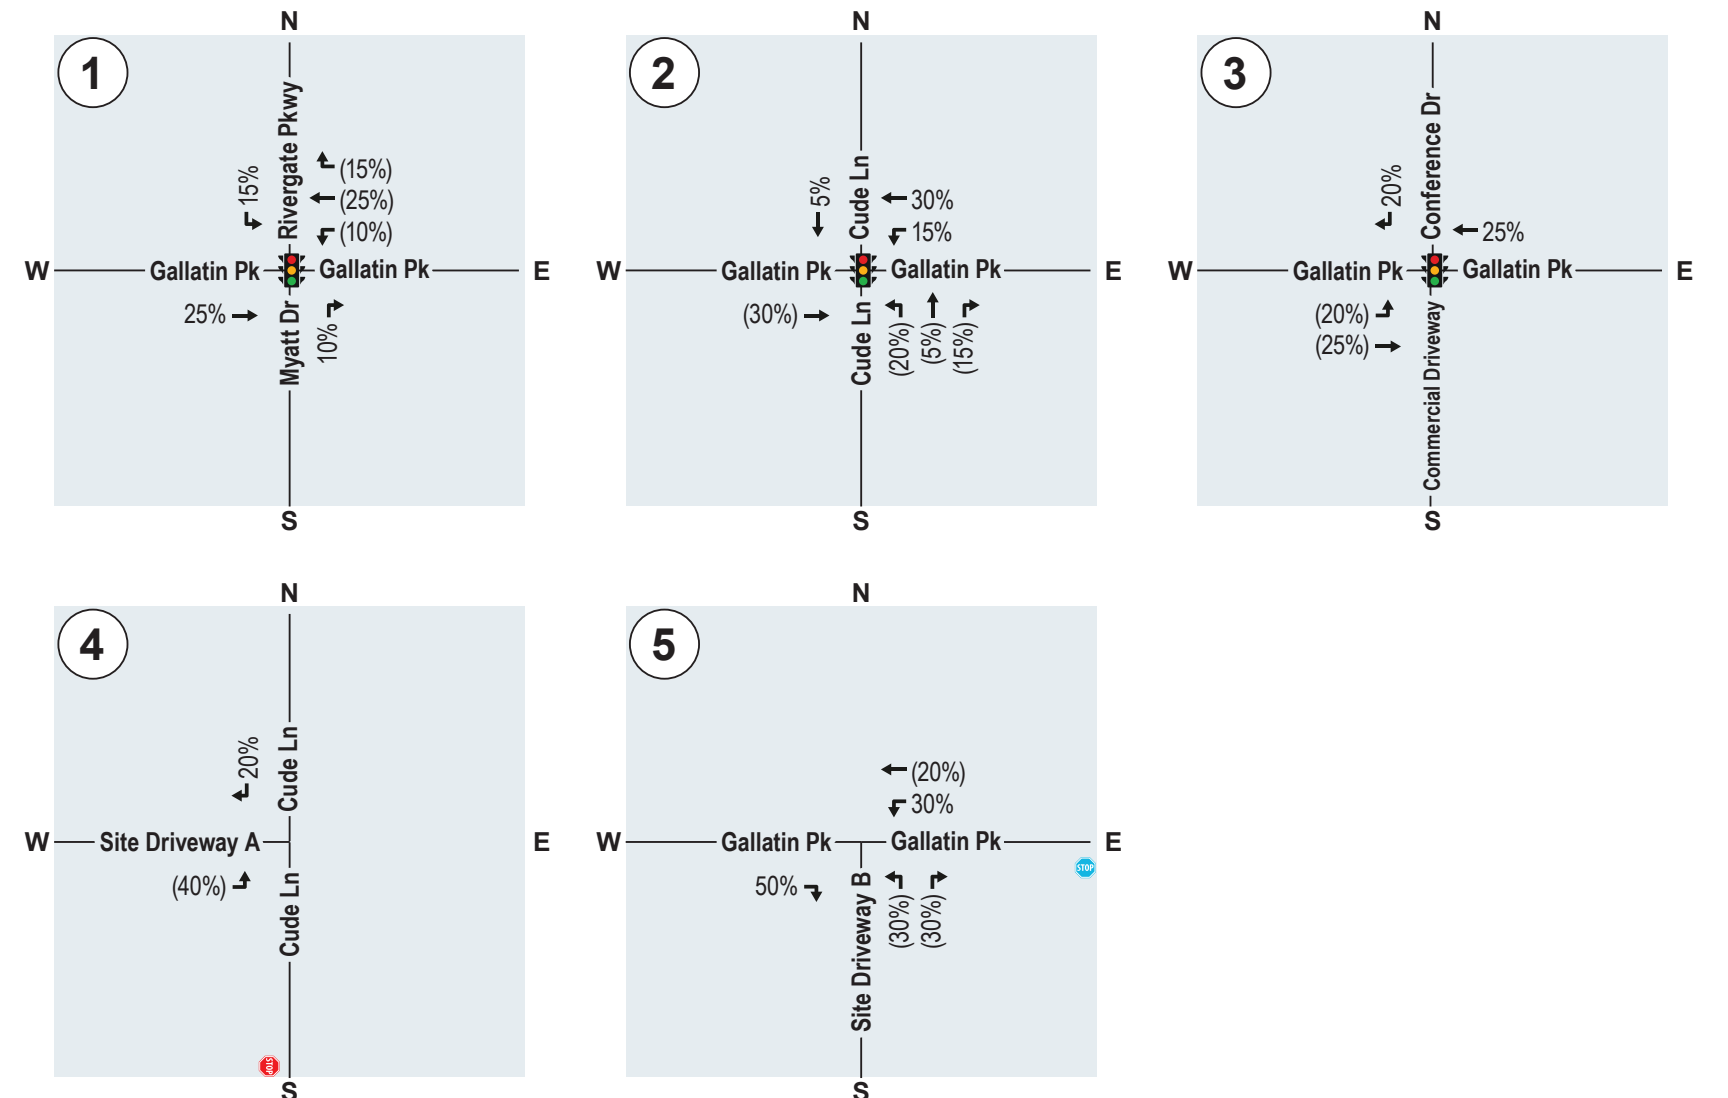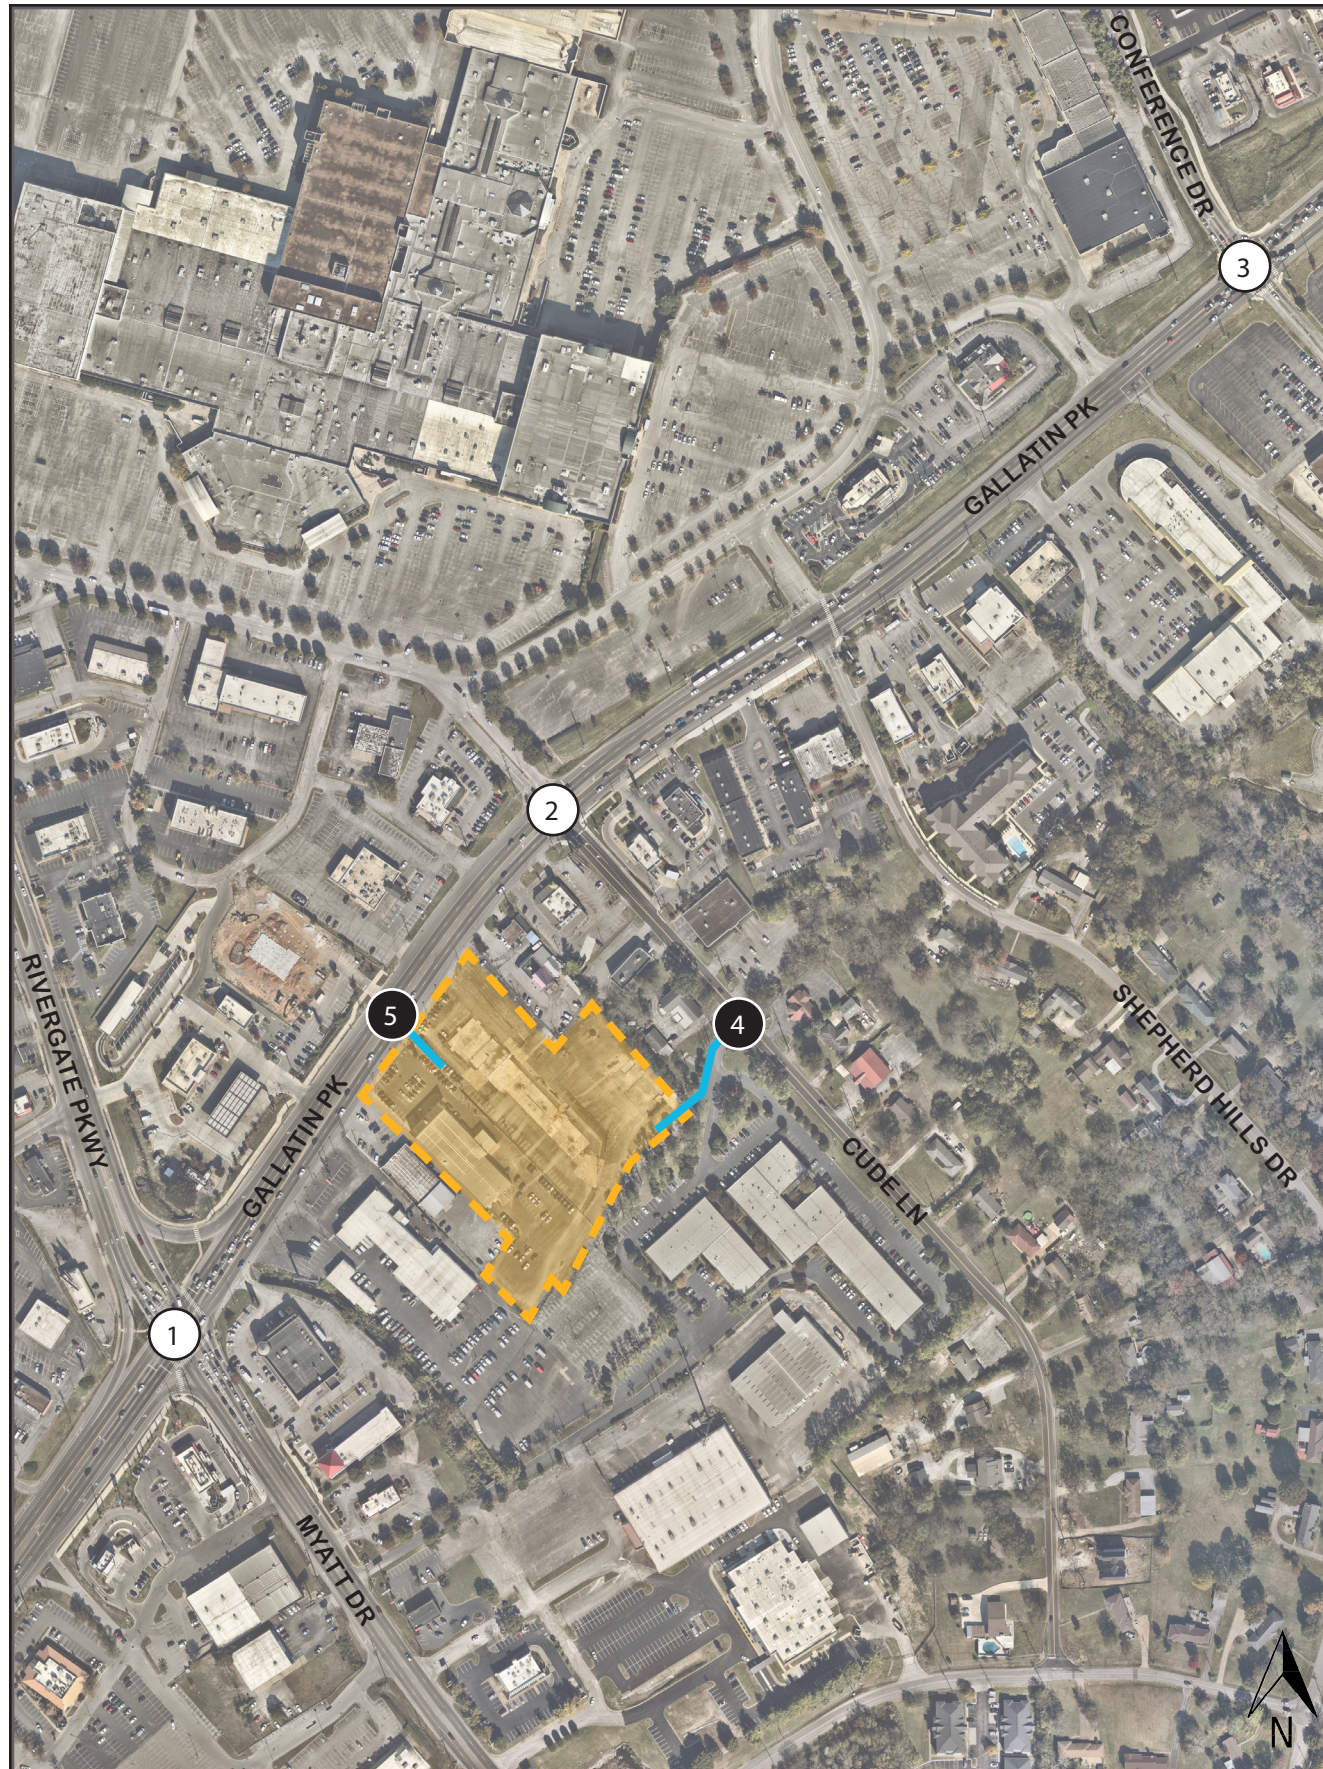



LEGEND	(X)	Signalized Intersection ID		Existing Traffic Signal	XX%	% Entering Distribution
	(X)	Unsignalized Intersection ID		Existing Stop Sign	(XX%)	% Exiting Distribution
	→	Turning Movement		Proposed Stop Sign		

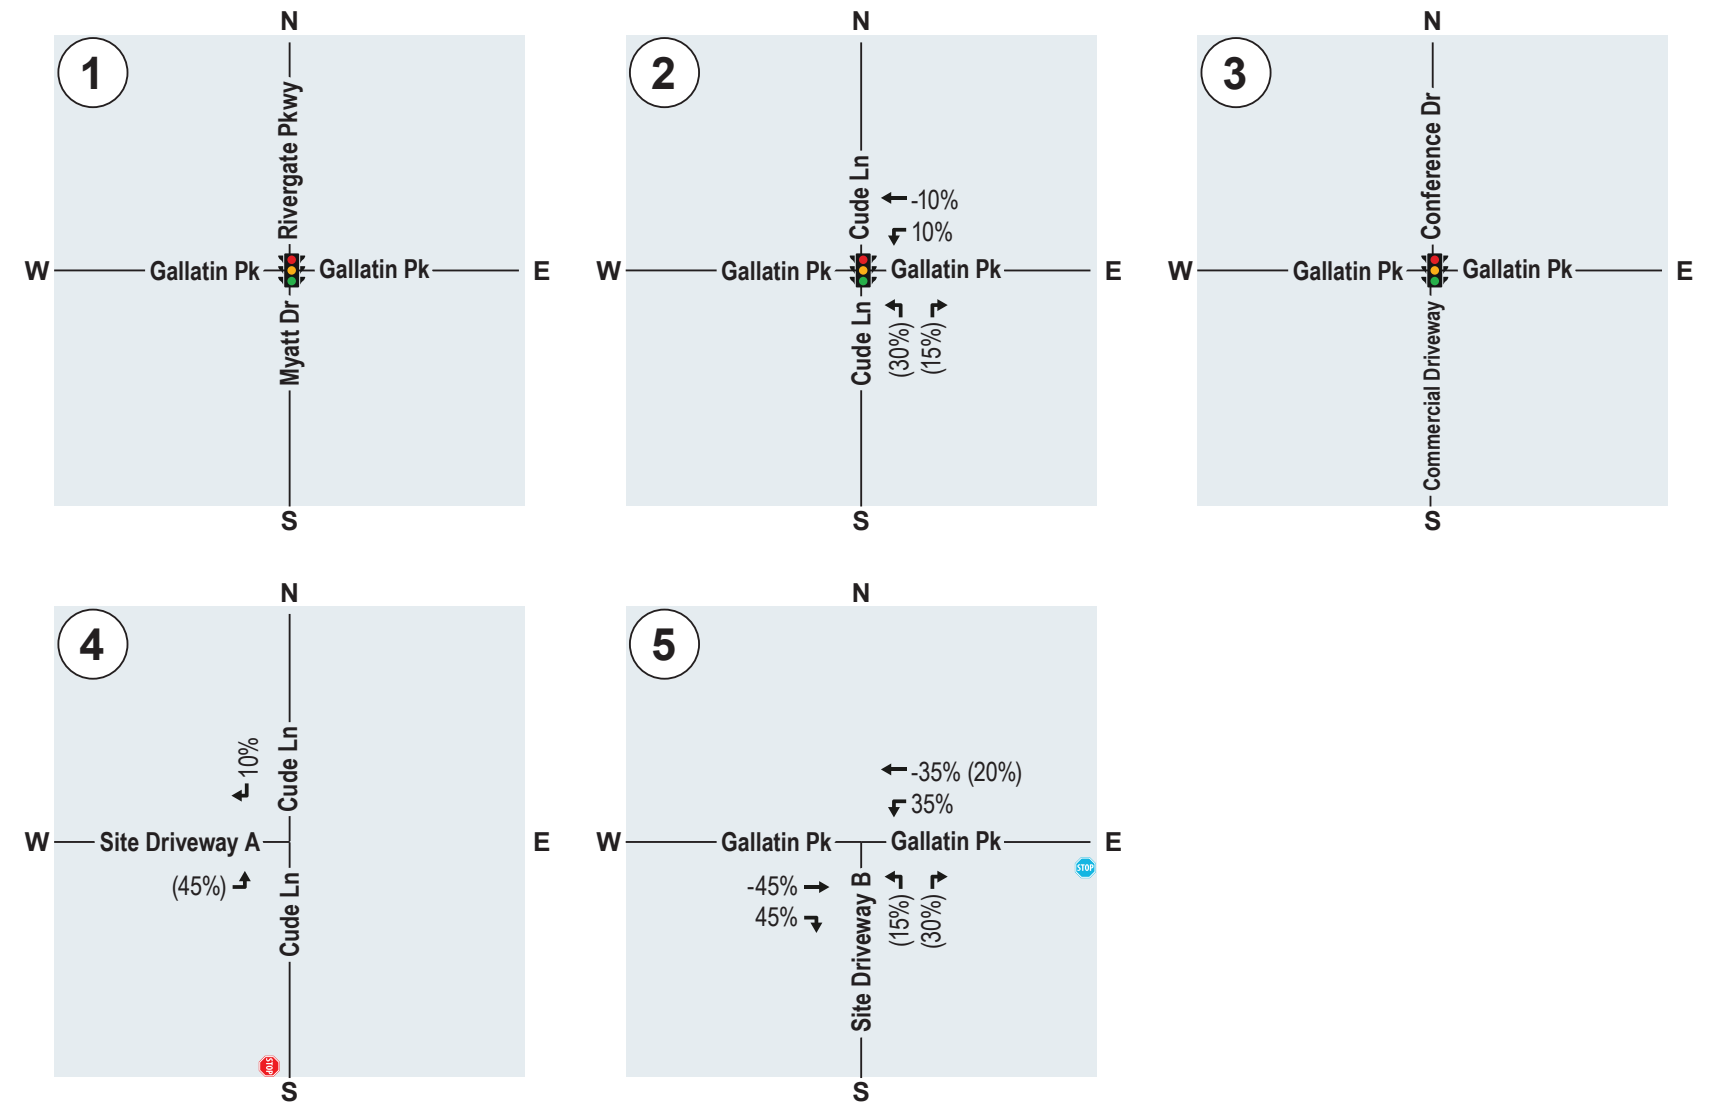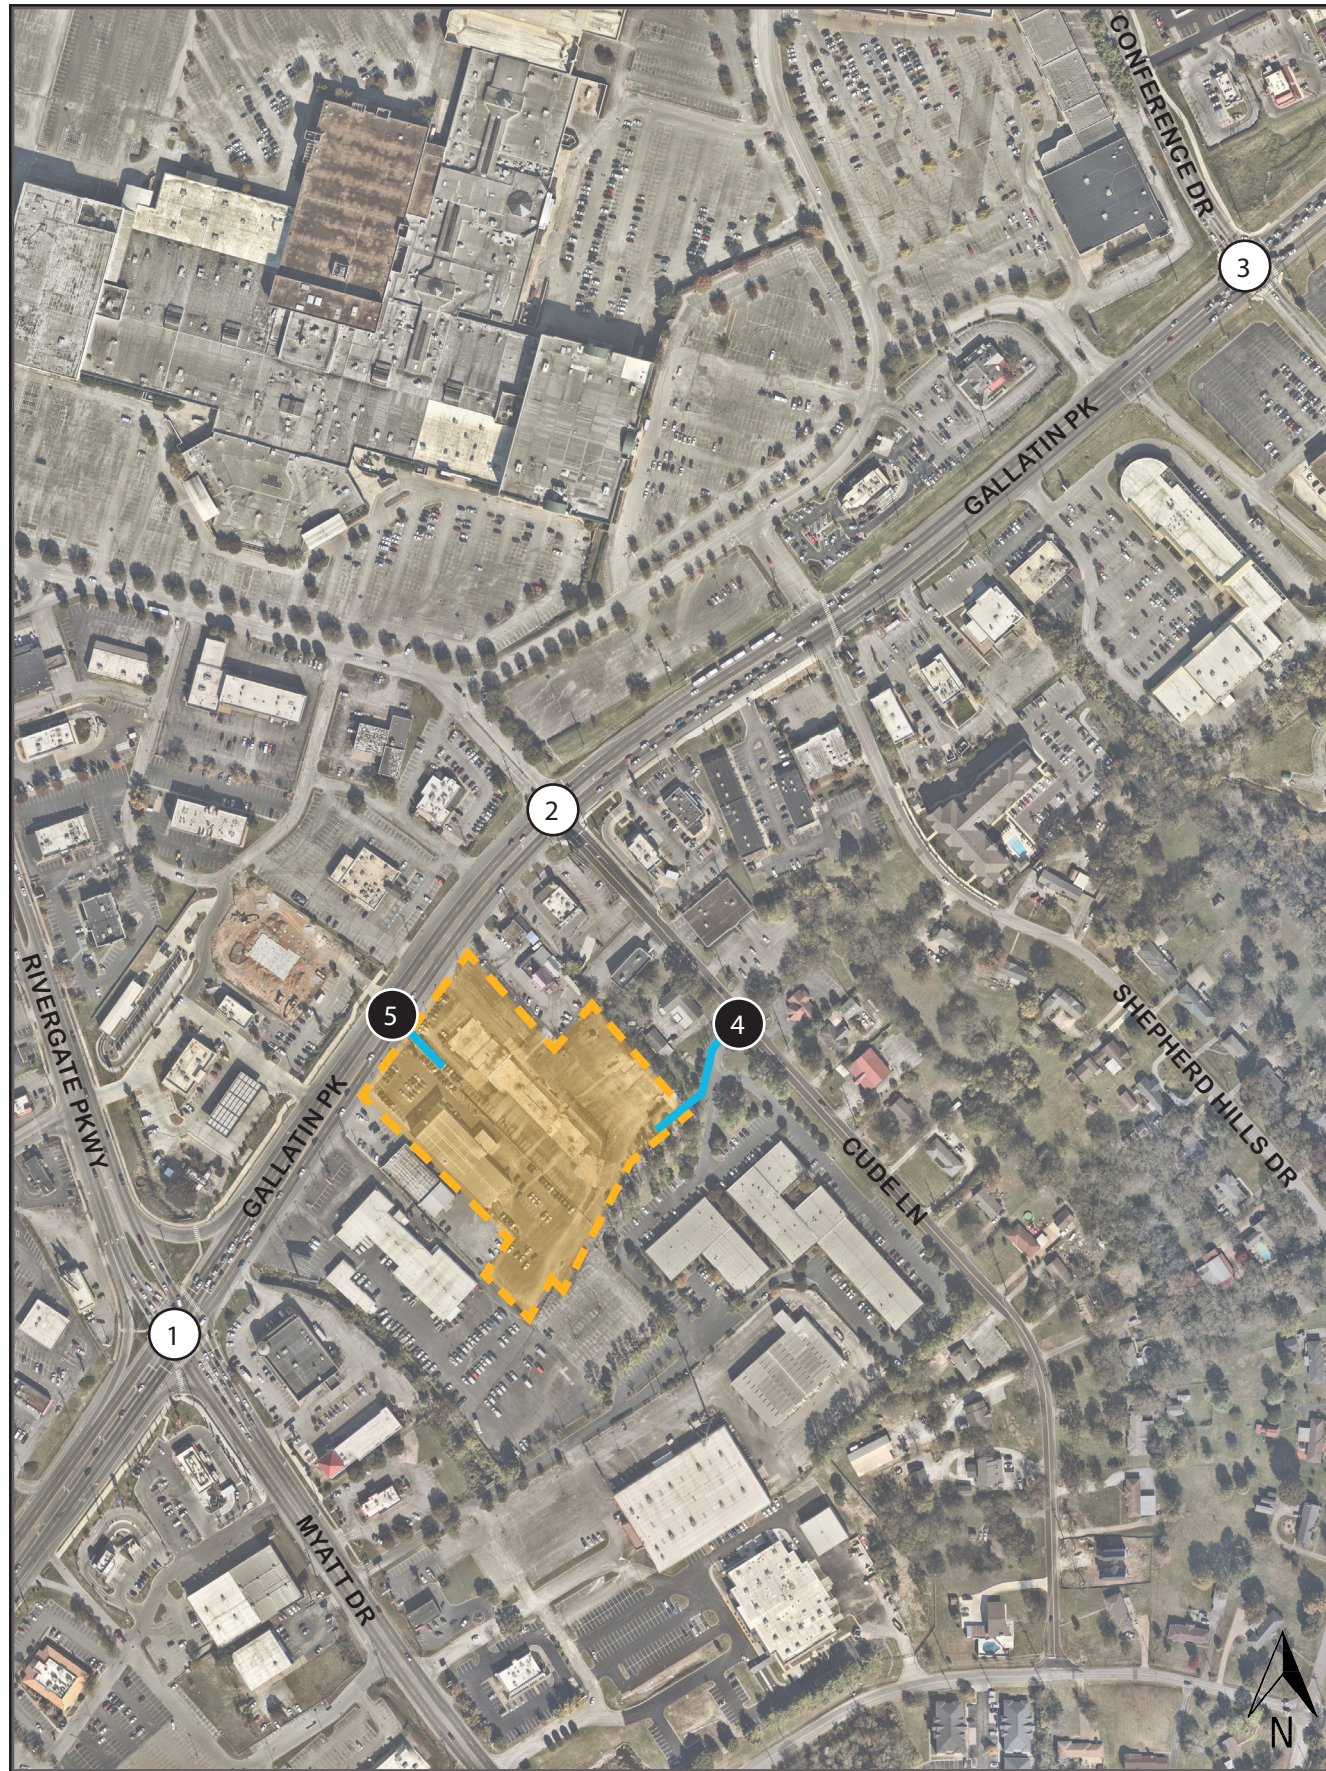



LEGEND		Signalized Intersection ID		Existing Traffic Signal	XX%	% Entering Distribution
		Unsignalized Intersection ID		Existing Stop Sign	(XX%)	% Exiting Distribution
		Turning Movement		Proposed Stop Sign		

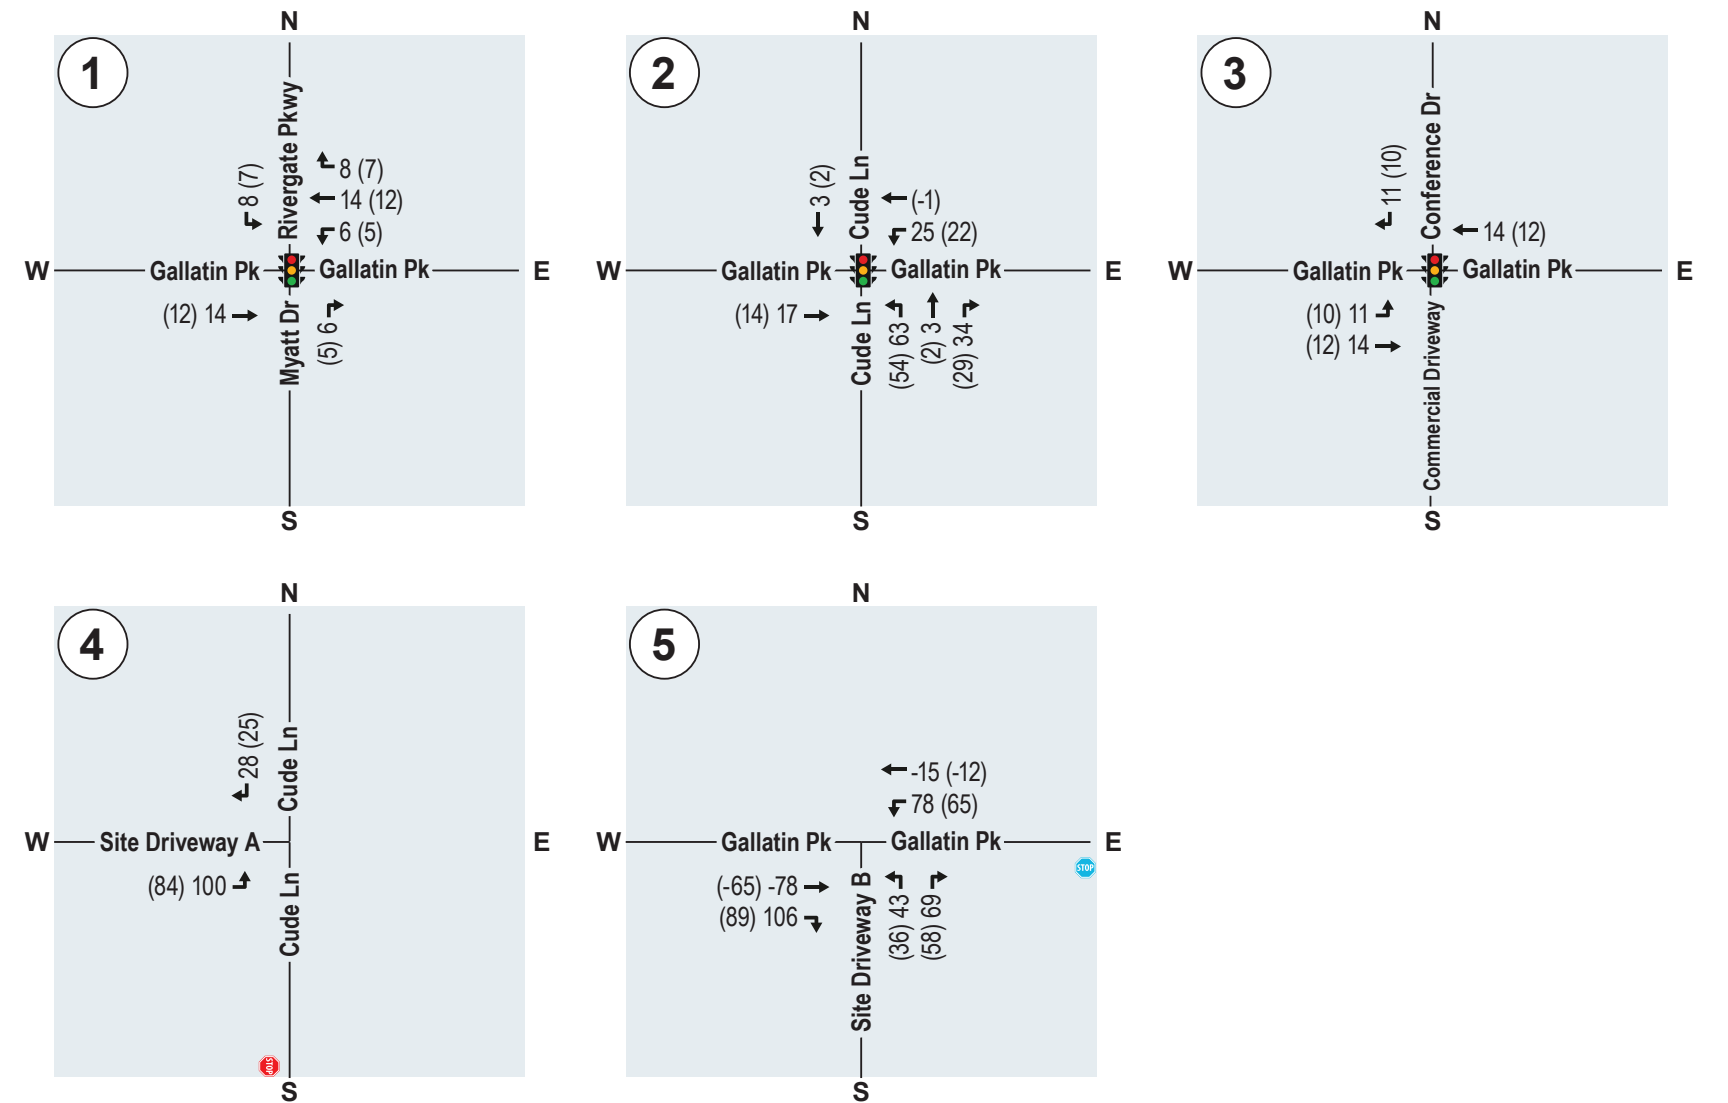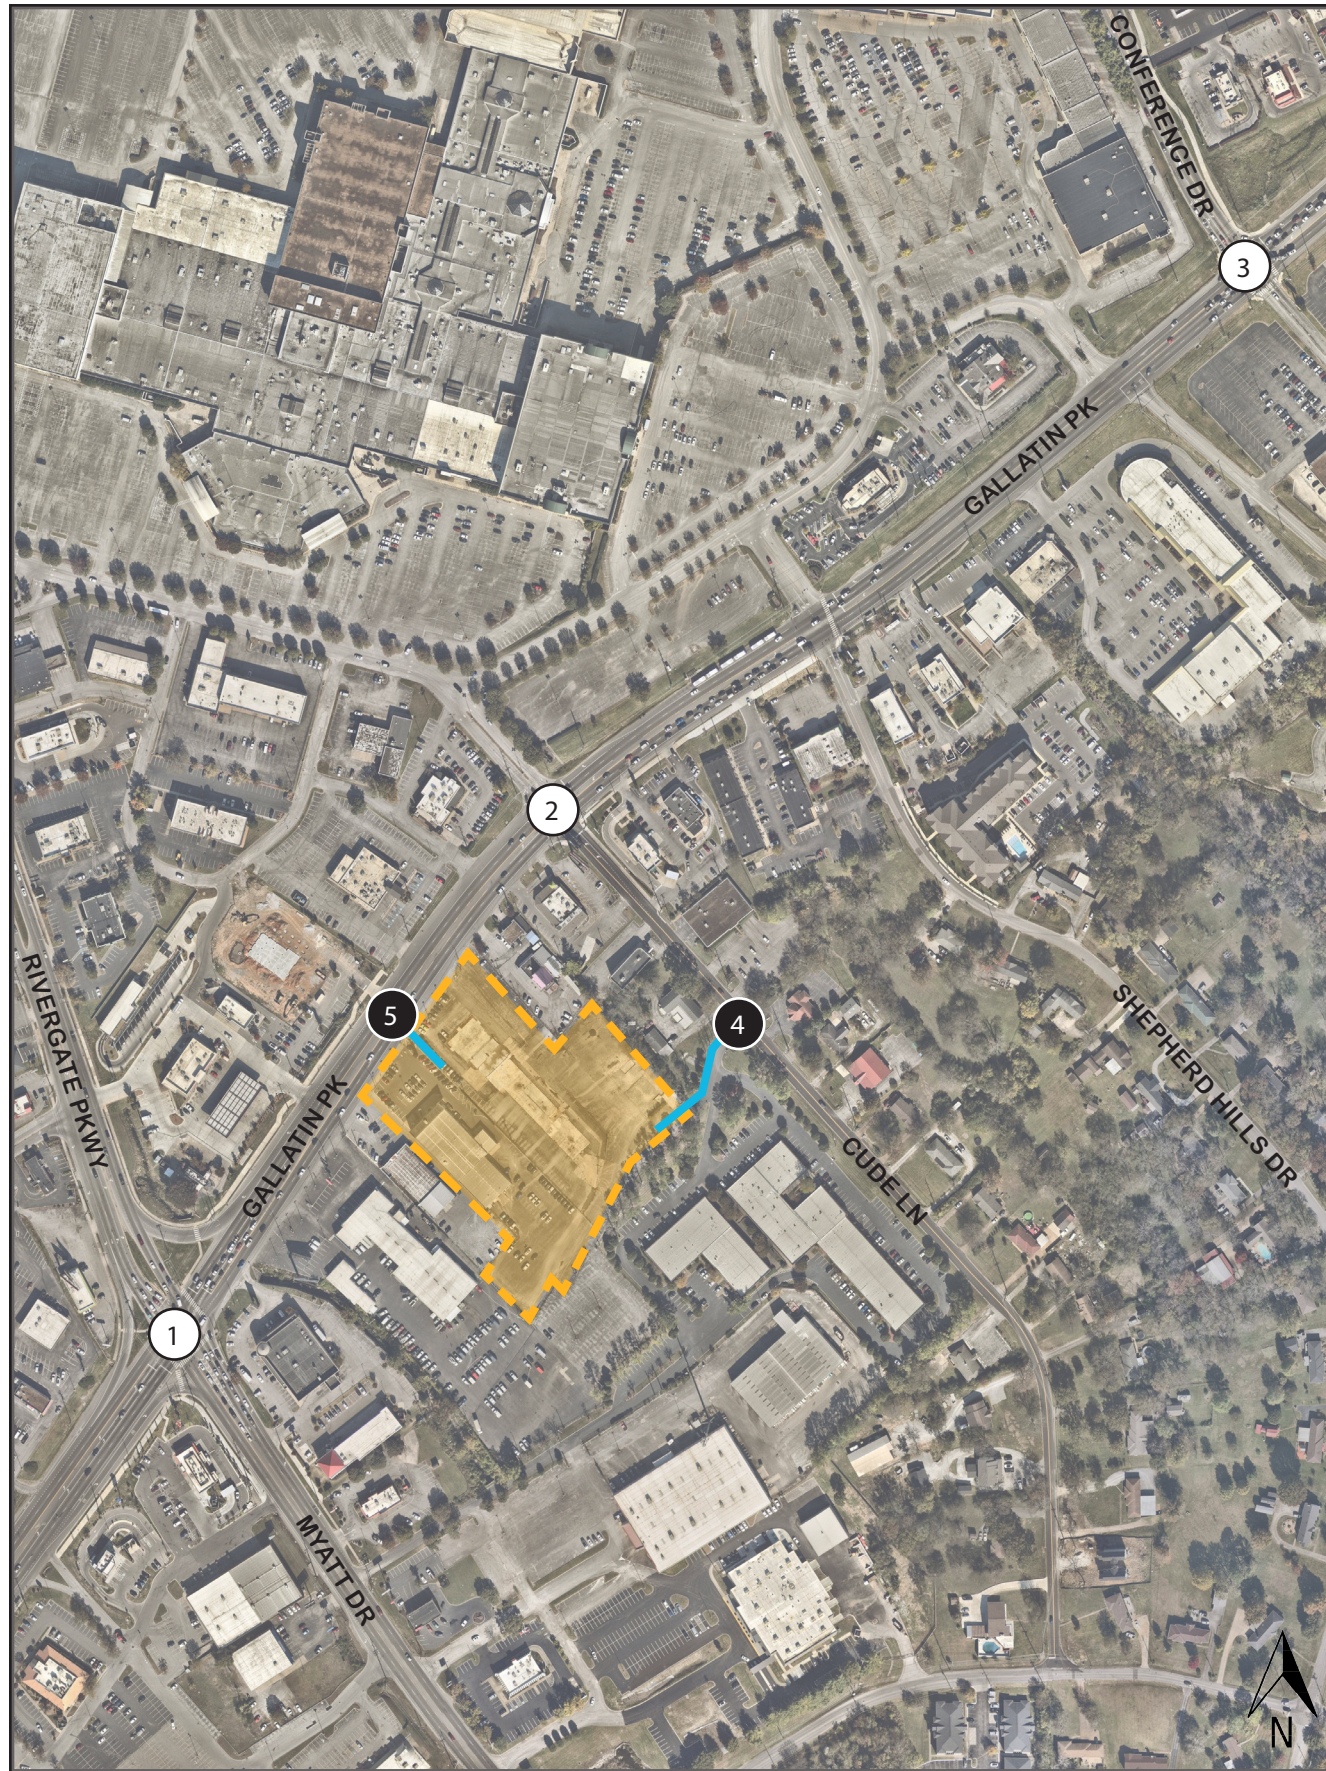

LEGEND		Signalized Intersection ID		Existing Traffic Signal	XX	AM Peak Hour Trips
		Unsignalized Intersection ID		Existing Stop Sign	(XX)	PM Peak Hour Trips
		Turning Movement		Proposed Stop Sign		

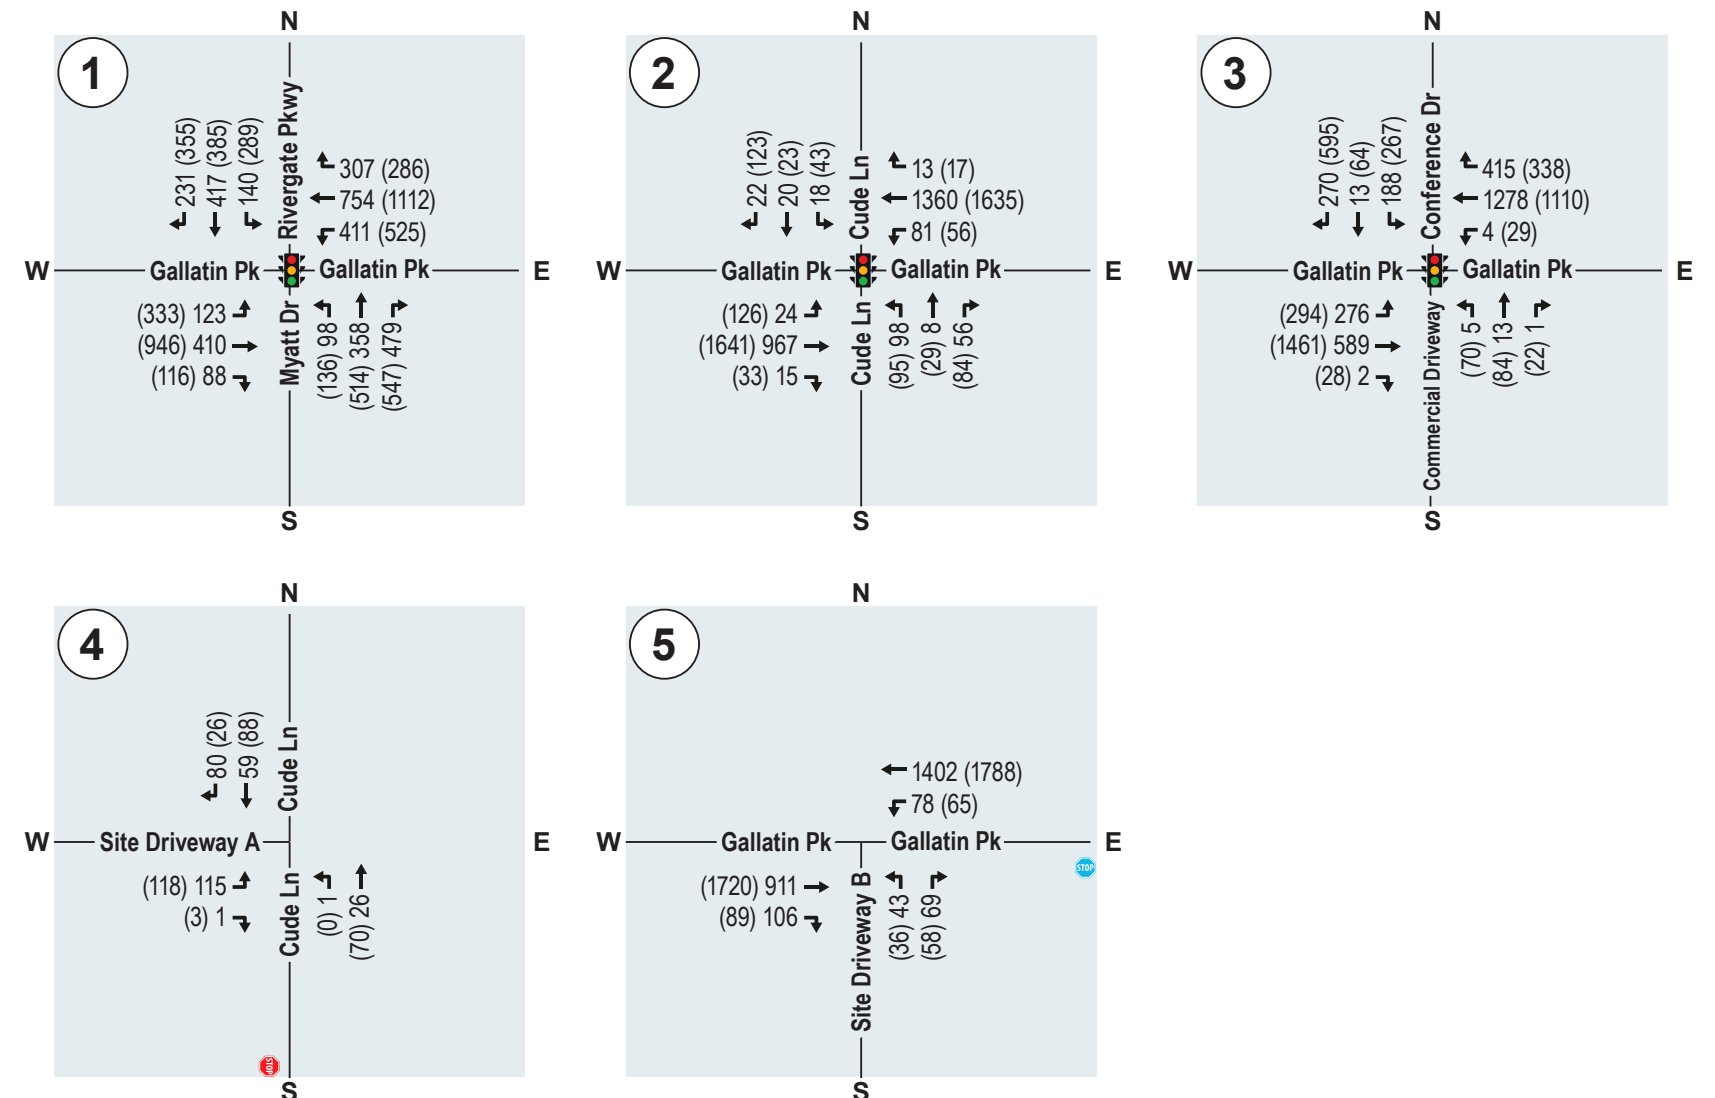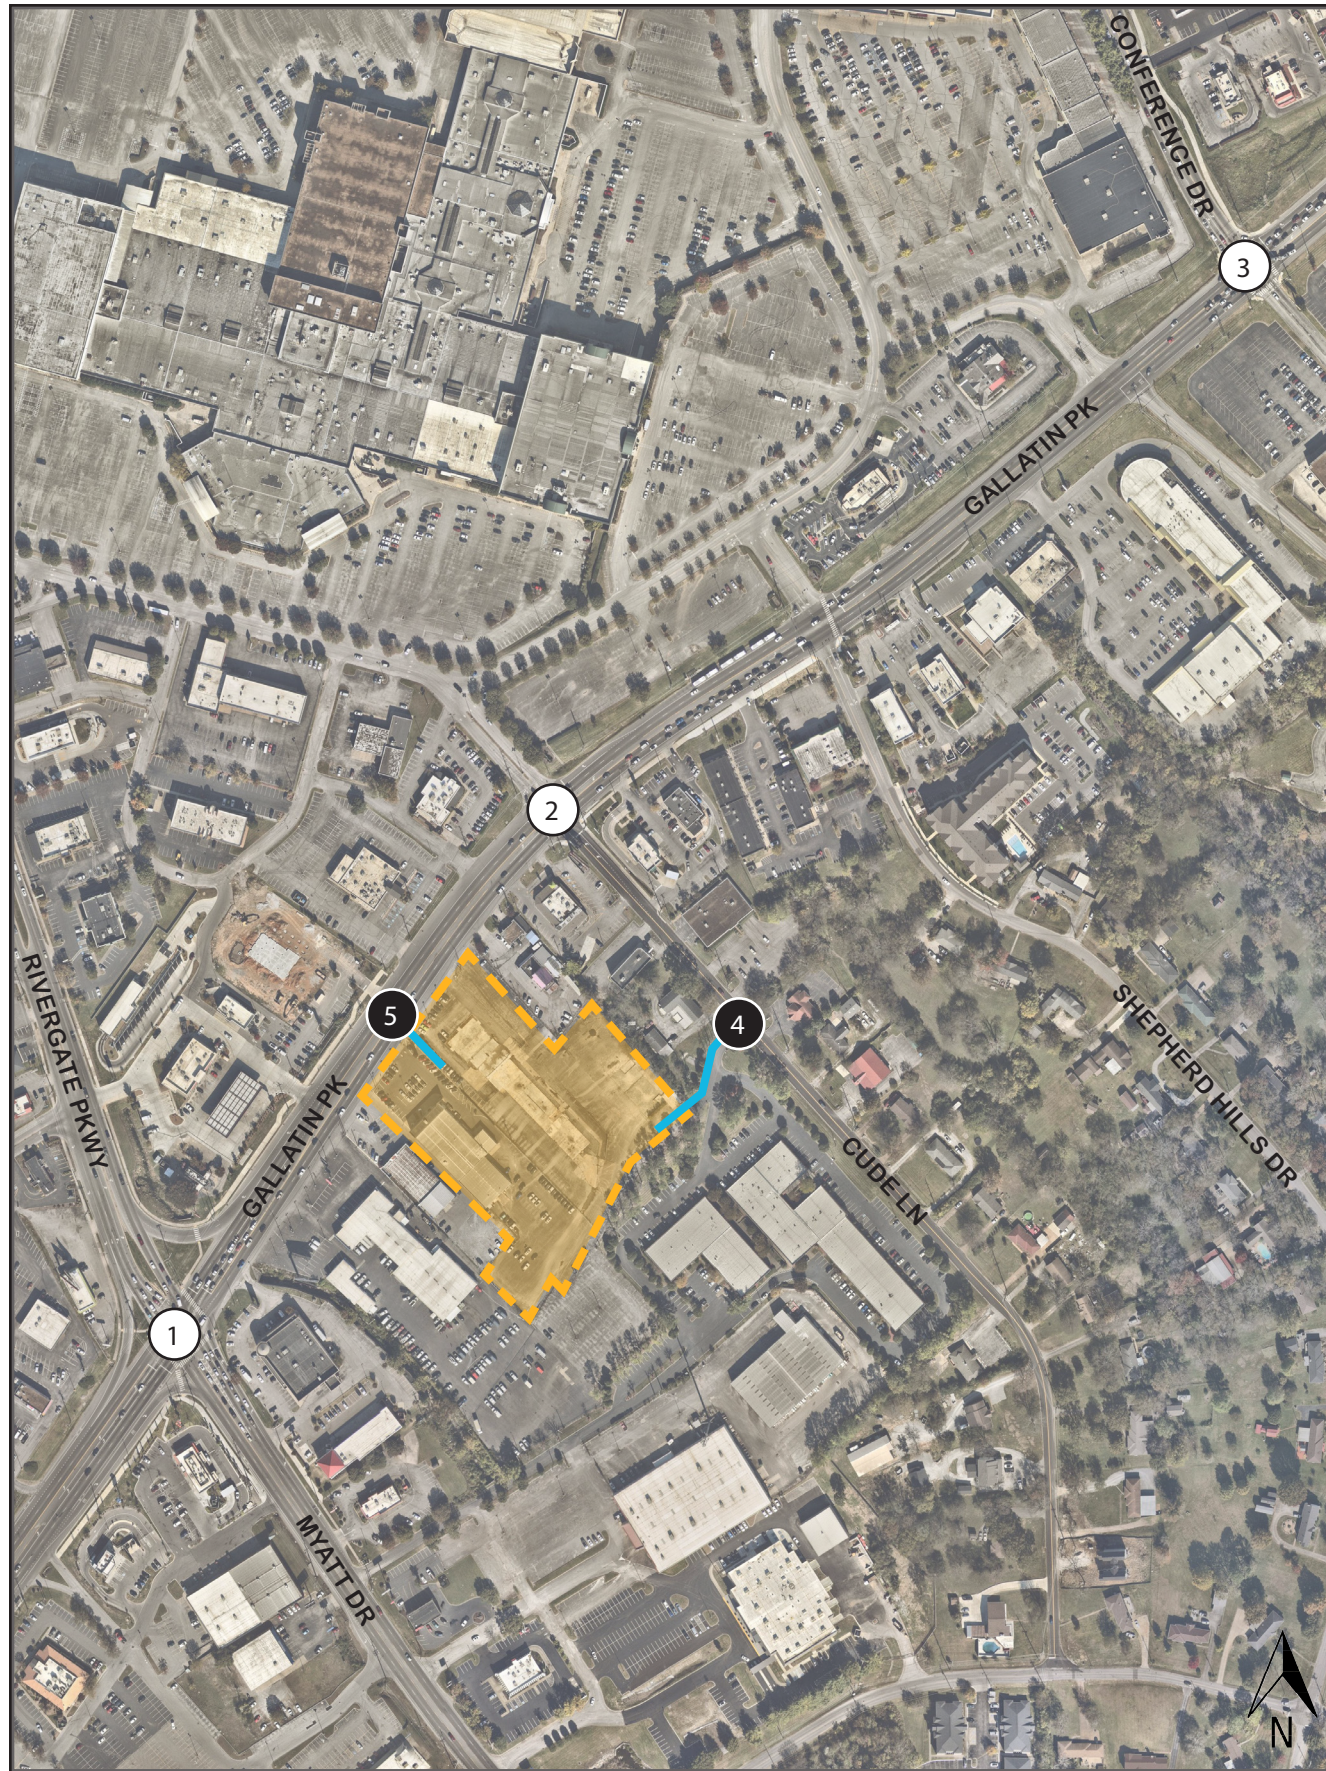

LEGEND		Signalized Intersection ID		Existing Traffic Signal	XX	AM Peak Hour Traffic Volumes
		Unsignalized Intersection ID		Existing Stop Sign	(XX)	PM Peak Hour Traffic Volumes
		Turning Movement		Proposed Stop Sign		

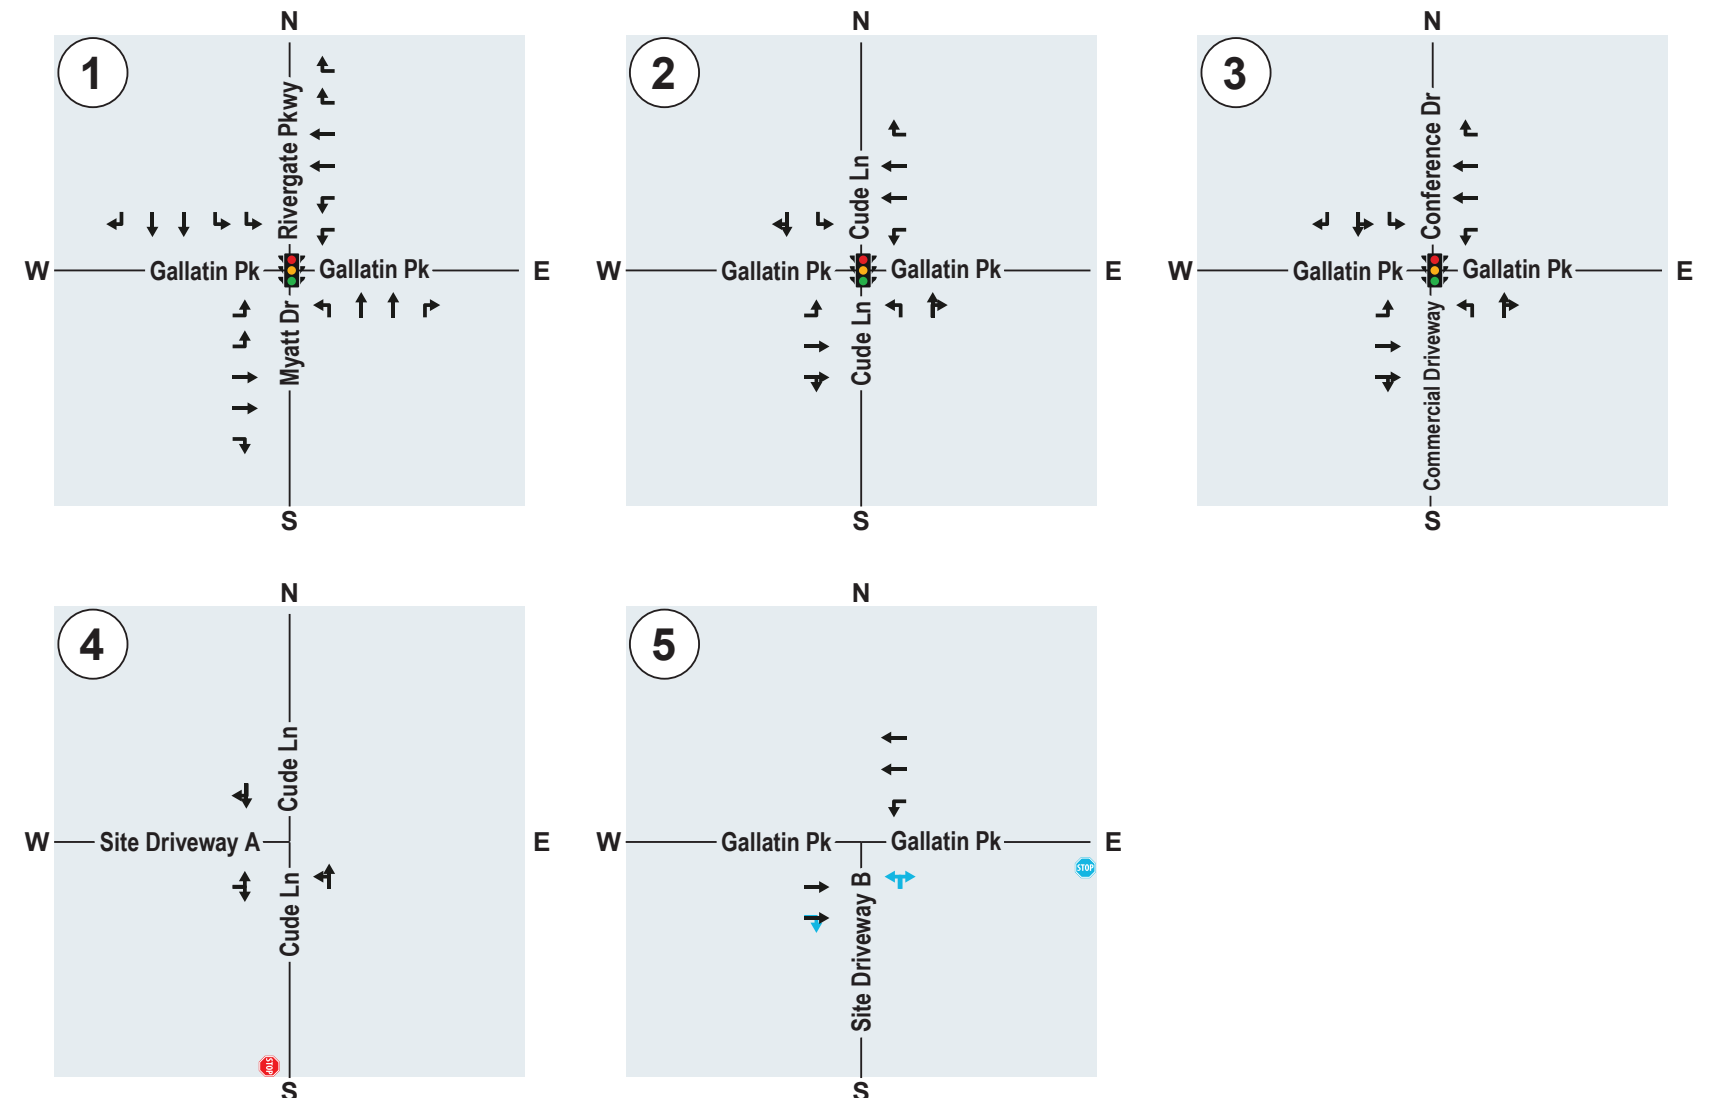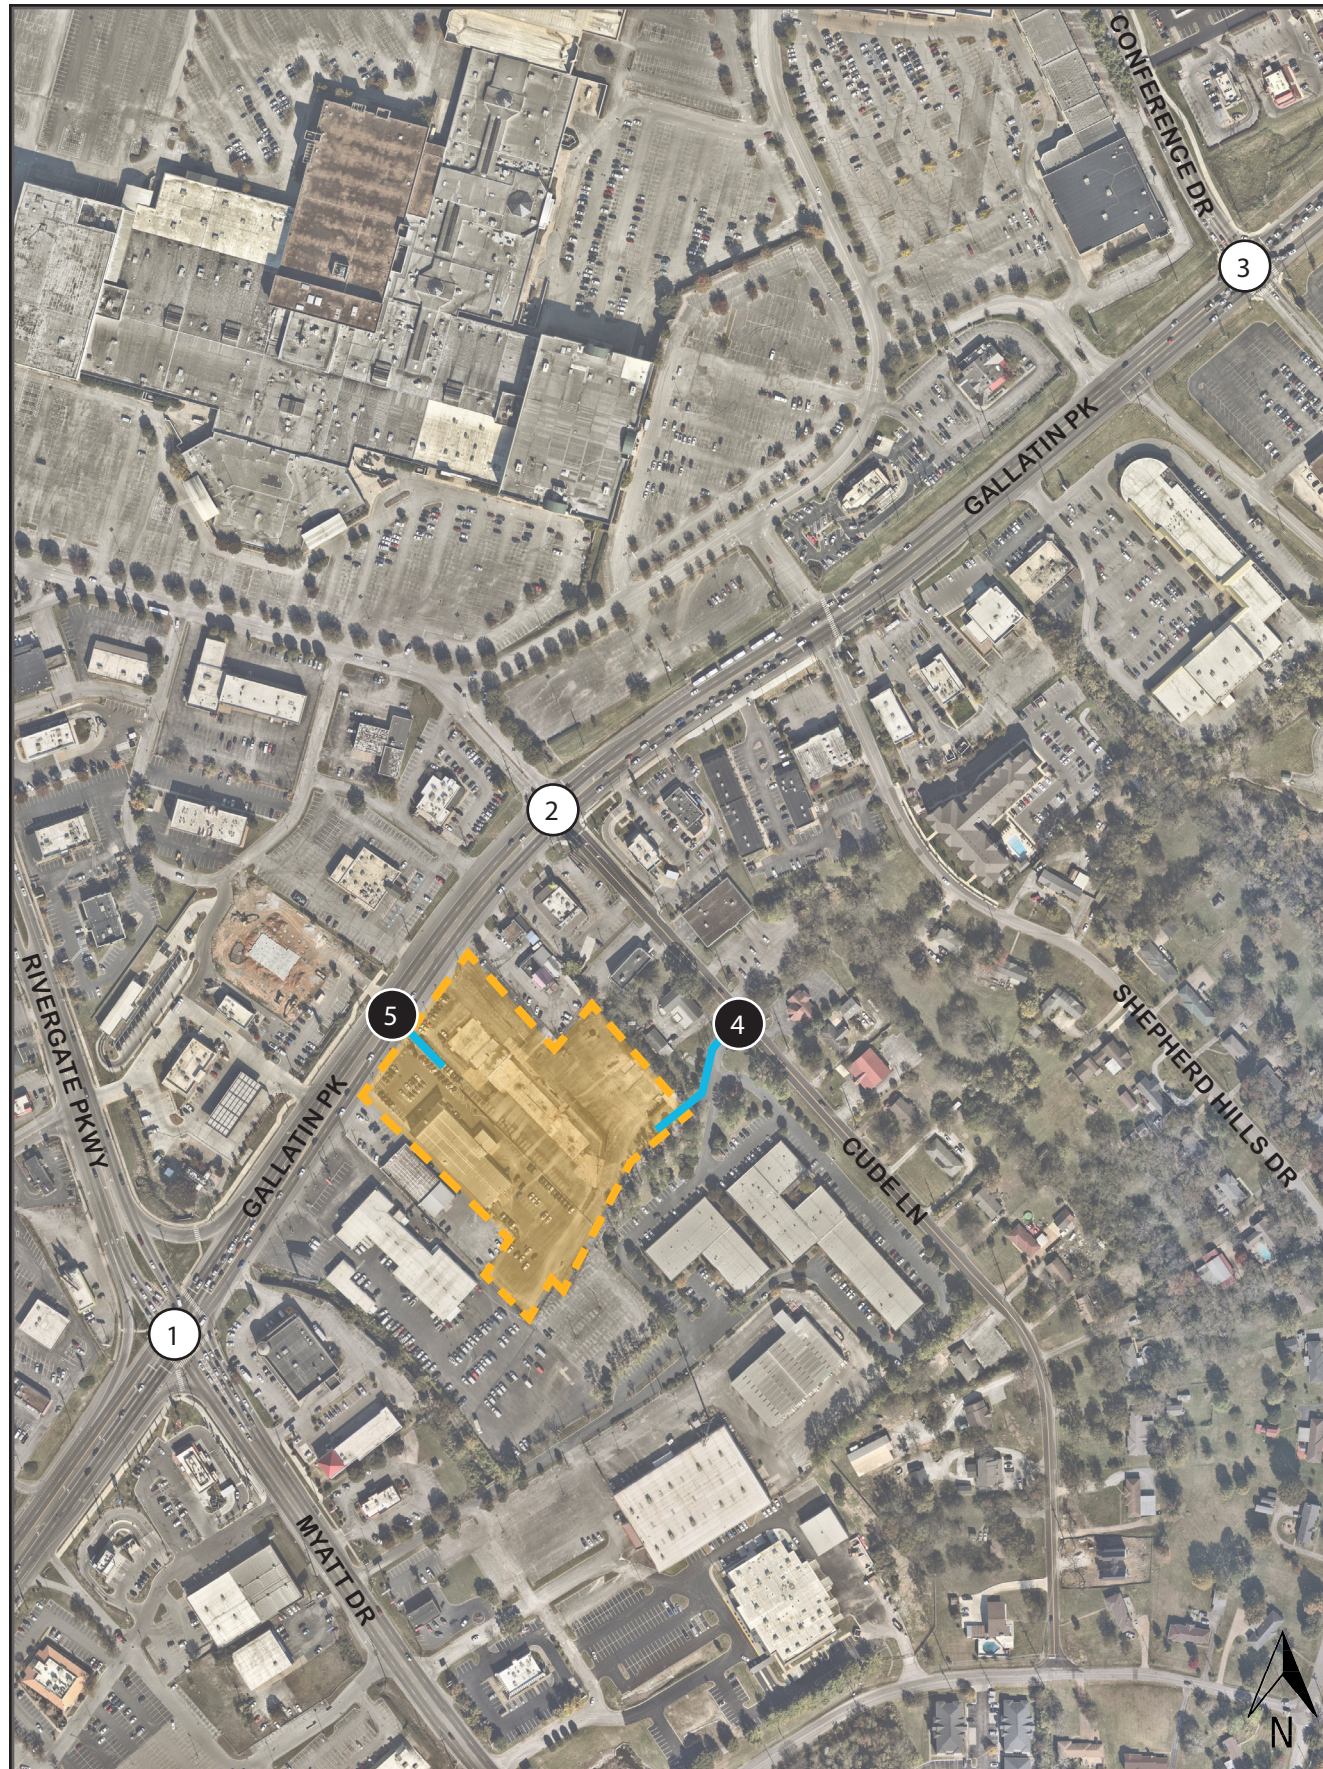

LEGEND			
(X)	Signalized Intersection ID		Existing Traffic Signal
(X)	Unsignalized Intersection ID		Existing Stop Sign
			Proposed Stop Sign
			Existing Lane Configuration
			Build Lane Configuration